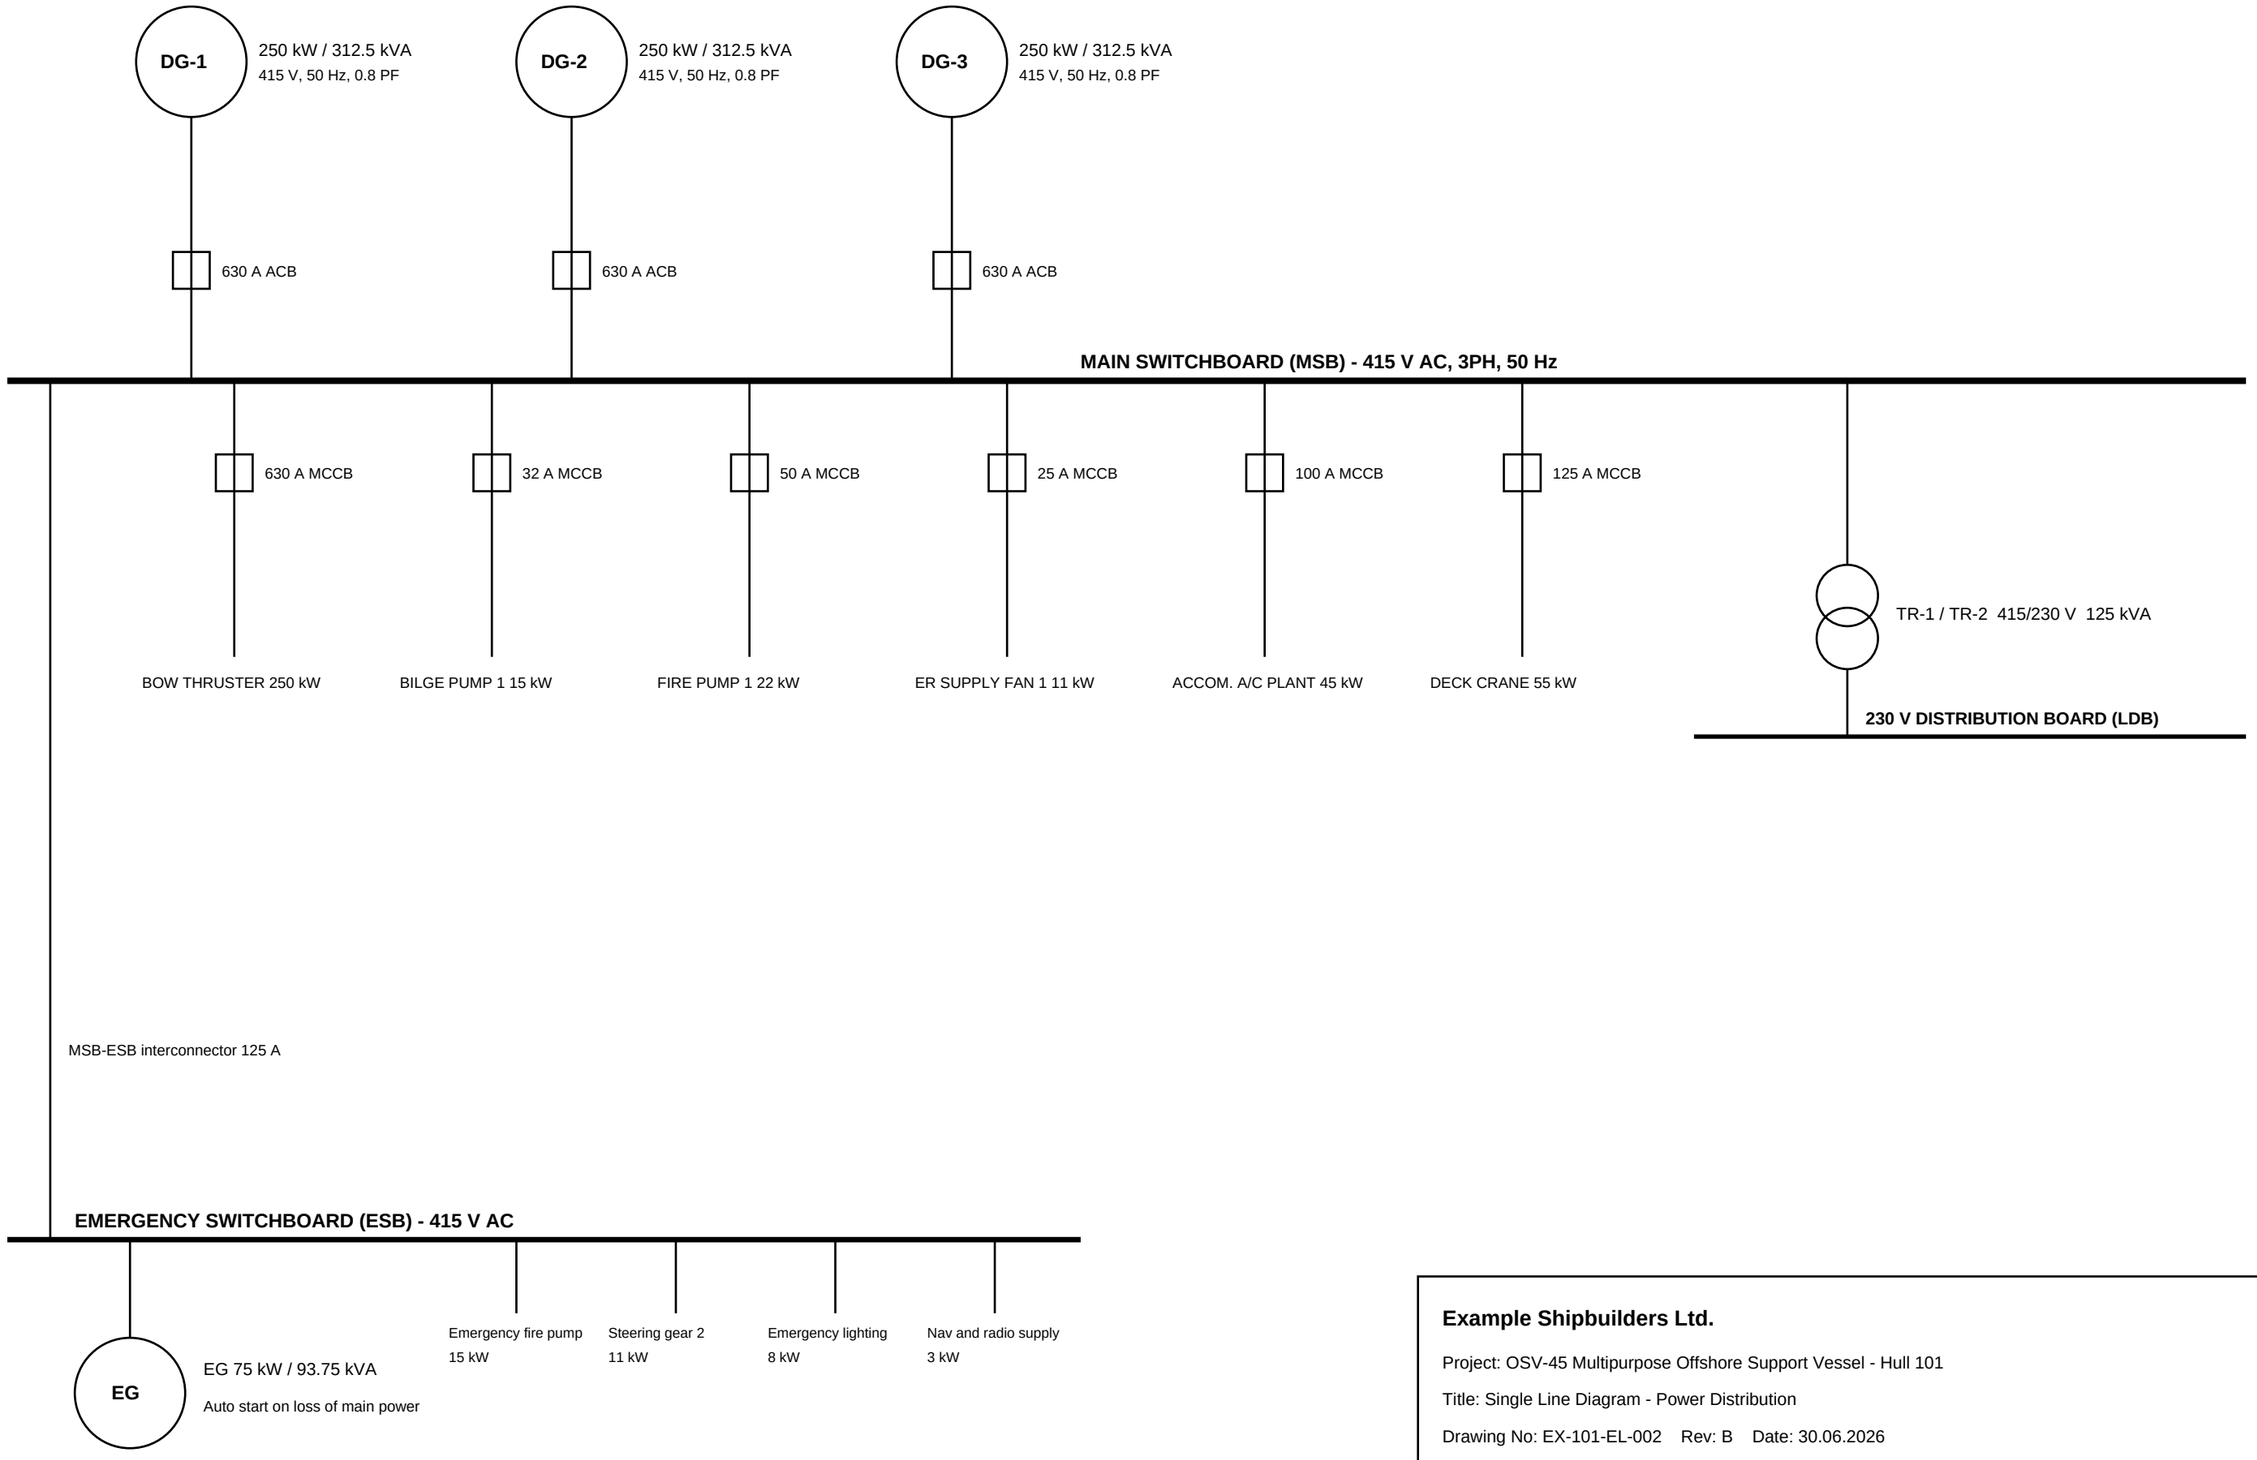

Example Shipbuilders Ltd.

Project: OSV-45 Multipurpose Offshore Support Vessel - Hull 101

Title: Single Line Diagram - Power Distribution

Drawing No: EX-101-EL-002 Rev: B Date: 30.06.2026

SAMPLE DOCUMENT - fictitious data for demonstration only